Projet d'aménagement paysager de

Mme et M

64160 MORLAAS

La fabrique de jardins
Laurence BAZEAU - Paysagiste conseil

laurenpaysage@gmail.com
07 72 43 27 00
www.lafabriquedejardins.fr
44190 Gorges

n°siret : 835 118 019 00016

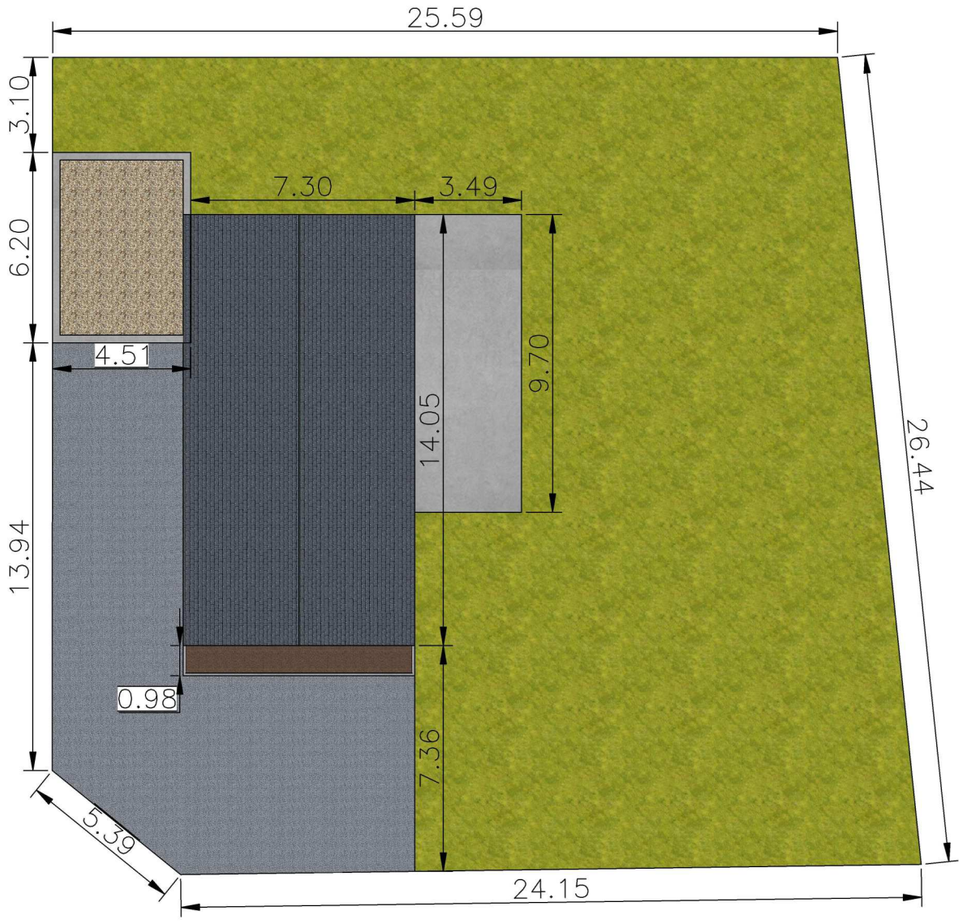

Descriptif du site - Souhaits des clients

Superficie : 500m² à Aménager

Environnement : Jardin de bourg

Les ambiances : Anglaise et Naturelle

La philosophie : Ecologique et permaculturelle pour le potager

Eléments à mettre en place : Potager - haie brise vue - espaces de jeux

Entretien du jardin : Jardin ne demandant pas d'entrerien (1 à 3h/mois)

	LA FABRIQUE DE JARDIN laurenpaysage@gmail.com www.lafabriquedejardins.fr	Projet de	- MORLAAS (64)	
	PLAN ETAT DES LIEUX	Dessiné par : Laurence.B	Date : 27/03/2018	Echelle : 1:200

Massif tropical
Haie libre brise vue
N
Potager
Massif d'hiver
Aire de jeux
Massif terre de bruyère
Massif bleu
Massif anglais
Projet de
- MORLAAS (64)
PLAN MASSE
Dessiné par : Laurence.B
LA FABRIQUE DE JARDIN
laurenpaysage@gmail.com
www.lafabriquedejardins.fr
Date : 27/03/2018
Echelle : 1:100

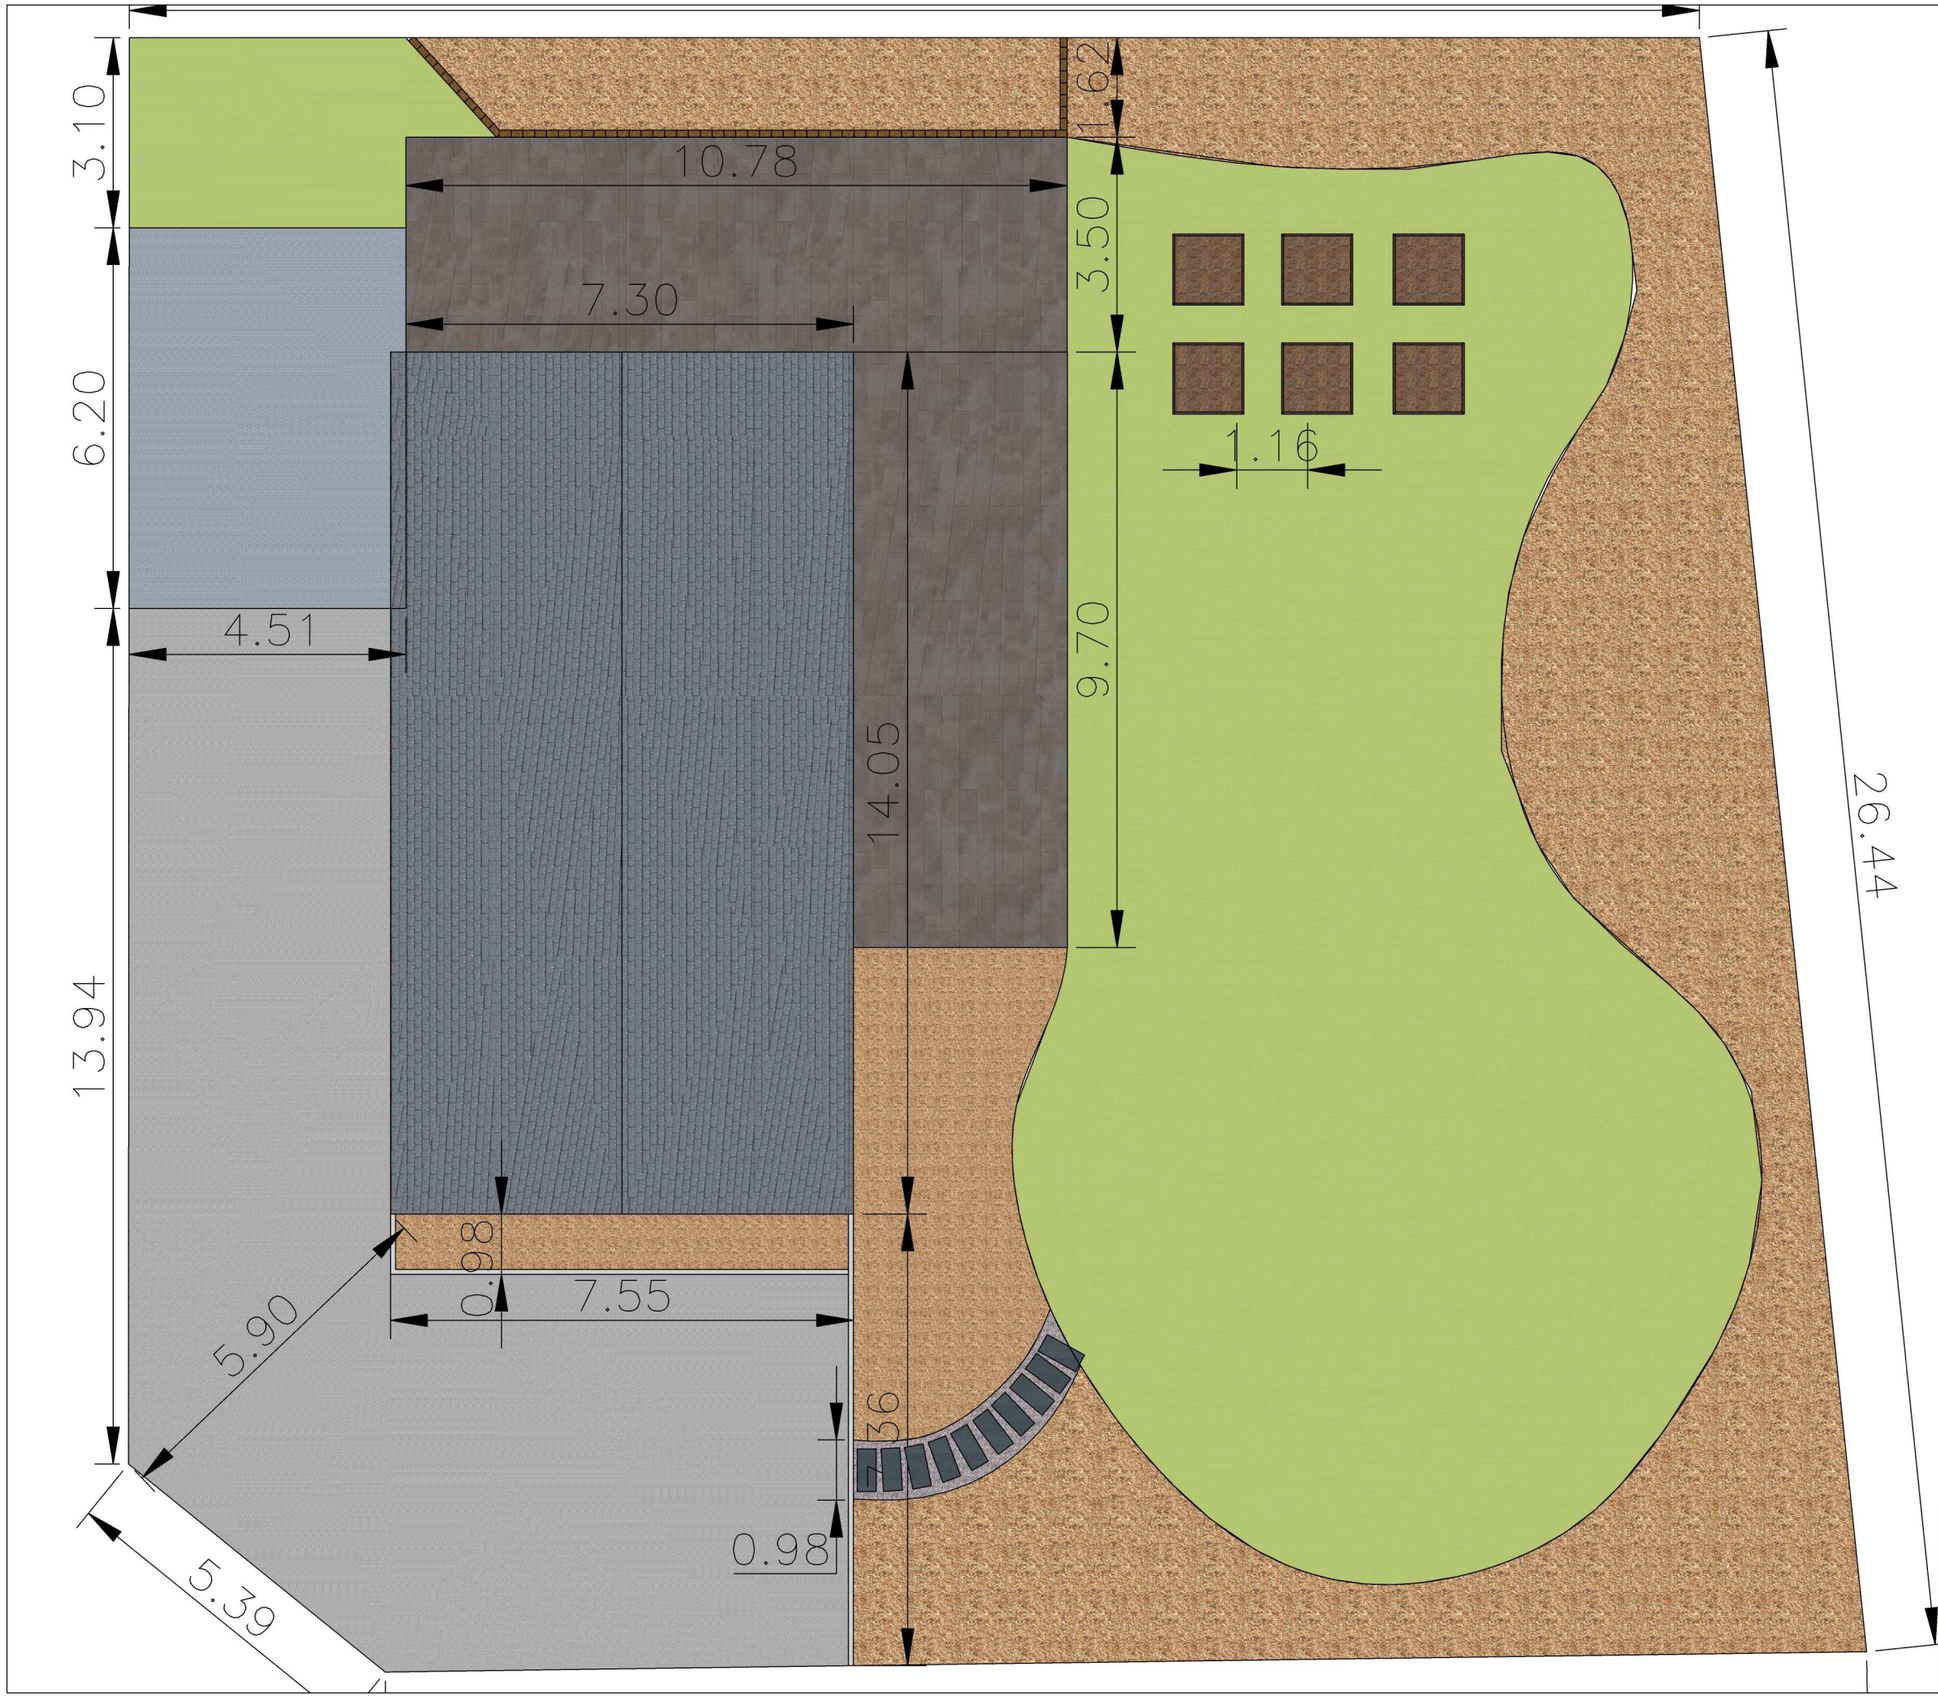

Projet de - MORLAAS (64)

PLAN METRES

Dessiné par : Laurence.B
LA FABRIQUE DE JARDIN
laurenpaysage@gmail.com
www.lafabriquedejardins.fr

Date : 27/03/2018

Echelle : 1:100

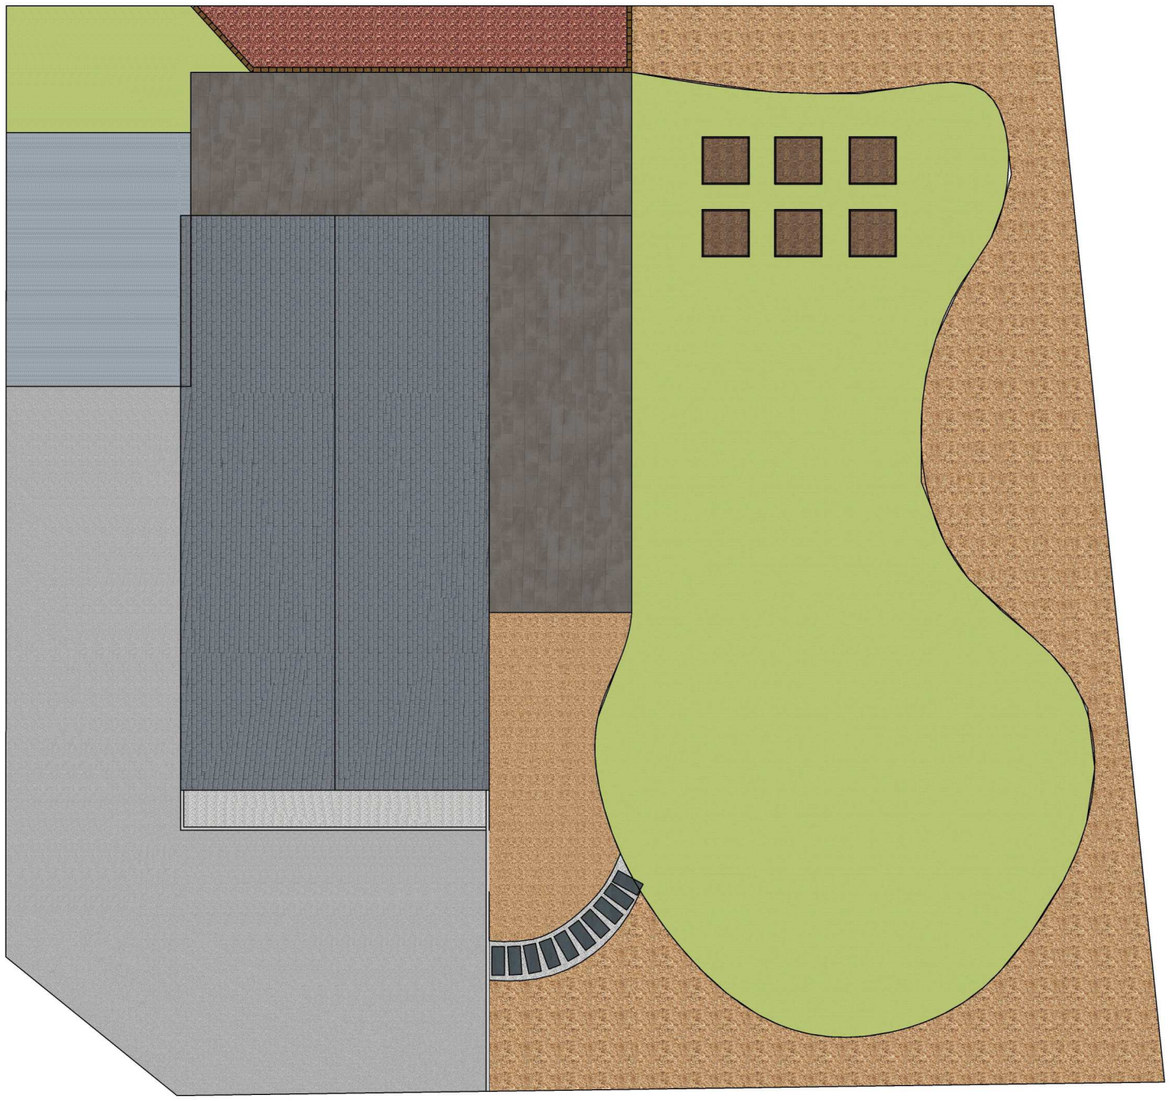

- Potager – 7,20 m²
- Paillage miscanthus sur toile tissée – 138,82 m²
- Gazon – 212,97 m²
- Bordures carrés potager – 27.6ml x 0.3m H
- Terrasse dalle de schistes – 71,55 m²
- Muret en traverses – 13.15ml
- Allée dalles de schiste – 2,14 m²
- Paillage gravier marbre blanc sur toile tissée – 9,10 m
- Paillage écorce de pin – 14,78 m²

	LA FABRIQUE DE JARDIN laurenpaysage@gmail.com www.lafabriquedejardins.fr	Projet de - MORLAAS (64)		
	PLAN DE REVETEMENT	Dessiné par : Laurence.B	Date : 27/03/2018	Echelle : 1:150

Détails plantations 6

Végétaux haie libre et arbres

1 Albizia julibrissin 'Ombrella',Acacia de Constantinople pleureur
1 Catalpa bignonioides,Catalpa commun
2 Acer campestre,Erable champêtre

1 Cercis siliquastrum,Arbre de Judée
1 Cornus kousa,Cornouiller du Japon
1 Acer ginnala,Erable du fleuve Amour
1 Magnolia x 'Susan',Magnolia à fleurs pourpres

10 Euonymus europaeus 'Red Cascade',Fusain d'Europe Red Cascade
8 Prunus lusitanica,Laurier du Portugal
8 Pittosporum tobira,Laurier-cerise
9 Sambucus nigra,Sureau noir
8 Viburnum tinus,Viorne tin

	LA FABRIQUE DE JARDIN laurenpaysage@gmail.com www.lafabriquedejardins.fr	Projet de	- MORLAAS (64)	
	PLAN PLANTATION	Dessiné par : Laurence.B	Date : 27/03/2018	Echelle : 1:100

Planche photos haie libre et arbres en isolés

Qté : 1

Albizia julibrissin 'Ombrella' - Acacia de

Qté : 1

Cercis siliquastrum - Arbre de Judée

Qté : 1

Catalpa bignonioides - Catalpa commun

Qté : 1

Cornus kousa - Cornouiller du Japon

Qté : 2

Acer campestre - Erable champêtre

Qté : 1

Acer ginnala - Erable du fleuve Amour

Qté : 10

Euonymus europaeus 'Red Cascade' - Fusain

Qté : 8

Prunus lusitanica - Laurier du Portugal

Qté : 8

Pittosporum tobira - Laurier-cerise

Qté : 1

Magnolia x 'Susan' - Magnolia à fleurs pourp

Qté : 9

Sambucus nigra - Sureau noir

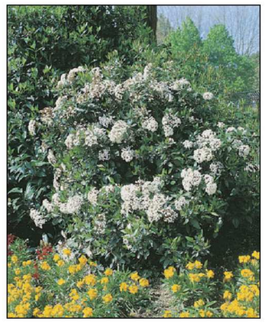

Qté : 8

Viburnum tinus - Viorne tin

	LA FABRIQUE DE JARDIN laurenpaysage@gmail.com www.lafabriquedejardins.fr	Projet de - MORLAAS (64)		
	Planche photo	Dessiné par : Laurence.B	Date : 27/03/2018	Echelle :

Détails plantations 2

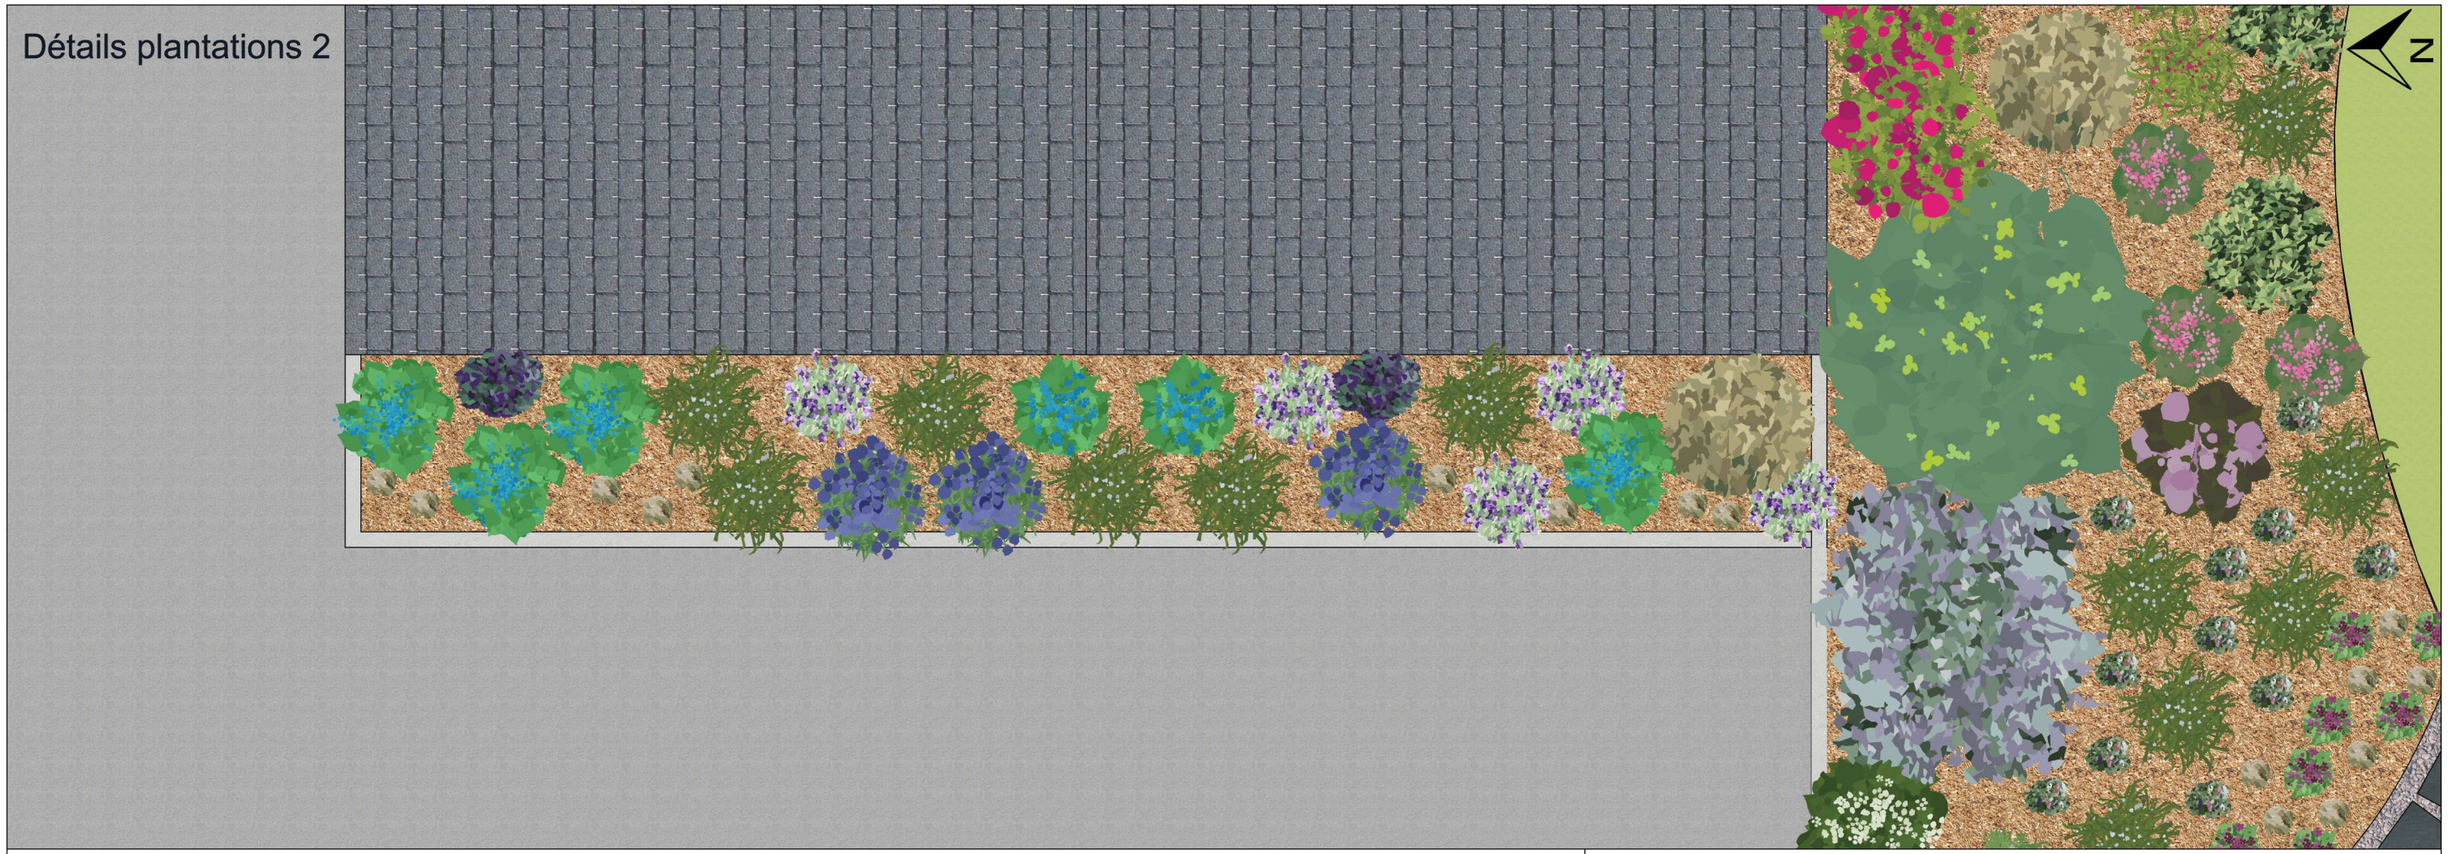

Végétaux massif bleu entrée

Qté : 4	Qté : 1	Qté : 9	Qté : 2
Agapanthus campanulatus – Agapanth	Stipa gigantea – Avoine géante	Stipa tenuifolia – Cheveux d'ange	Clematis 'Jackmanii' – Clématite Jackmanii
Qté : 6	Qté : 2	Qté : 3	Qté : 5
Pennisetum orientale – Herbe aux écouvillons	Salvia uliginosa – Sauge	Salvia nemorosa – Sauge des bois	Verbena bonariensis – Verveine de Buenos–Aire

Végétaux massif bleu entrée

4 Agapanthus campanulatus,Agapanthe campanulée
1 Stipa gigantea,Avoine géante
9 Stipa tenuifolia,Cheveux d'ange
2 Clematis 'Jackmanii',Clématite Jackmanii
6 Pennisetum orientale,Herbe aux écouvillons
2 Salvia uliginosa,Sauge
3 Salvia nemorosa,Sauge des bois
5 Verbena bonariensis,Verveine de Buenos–Aires

	LA FABRIQUE DE JARDIN laurenpaysage@gmail.com www.lafabriquedejardins.fr	Projet de	- MORLAAS (64)	
	MASSIF ENTREE	Dessiné par : Laurence.B	Date : 27/03/2018	Echelle : 1:25

L'entrée - Camaïeu de bleu associé à la douceur des graminées

GALET MARBRE BLANC

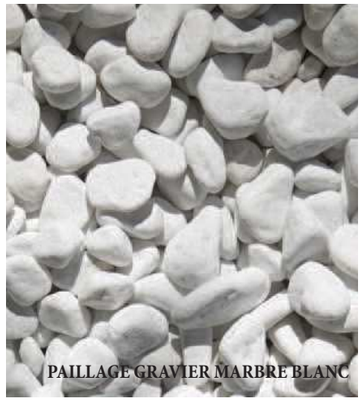

PAILLAGE GRAVIER MARBRE BLANC

Projet d'aménagement paysager de
Mme et M
64160 MORLAAS

Planche ambiance 1

Laurence BAZEAU
07 72 43 27 00
laurenpaysage@gmail.fr

www.lafabriquedejardins.fr

n°siret : 835 118 019 00016

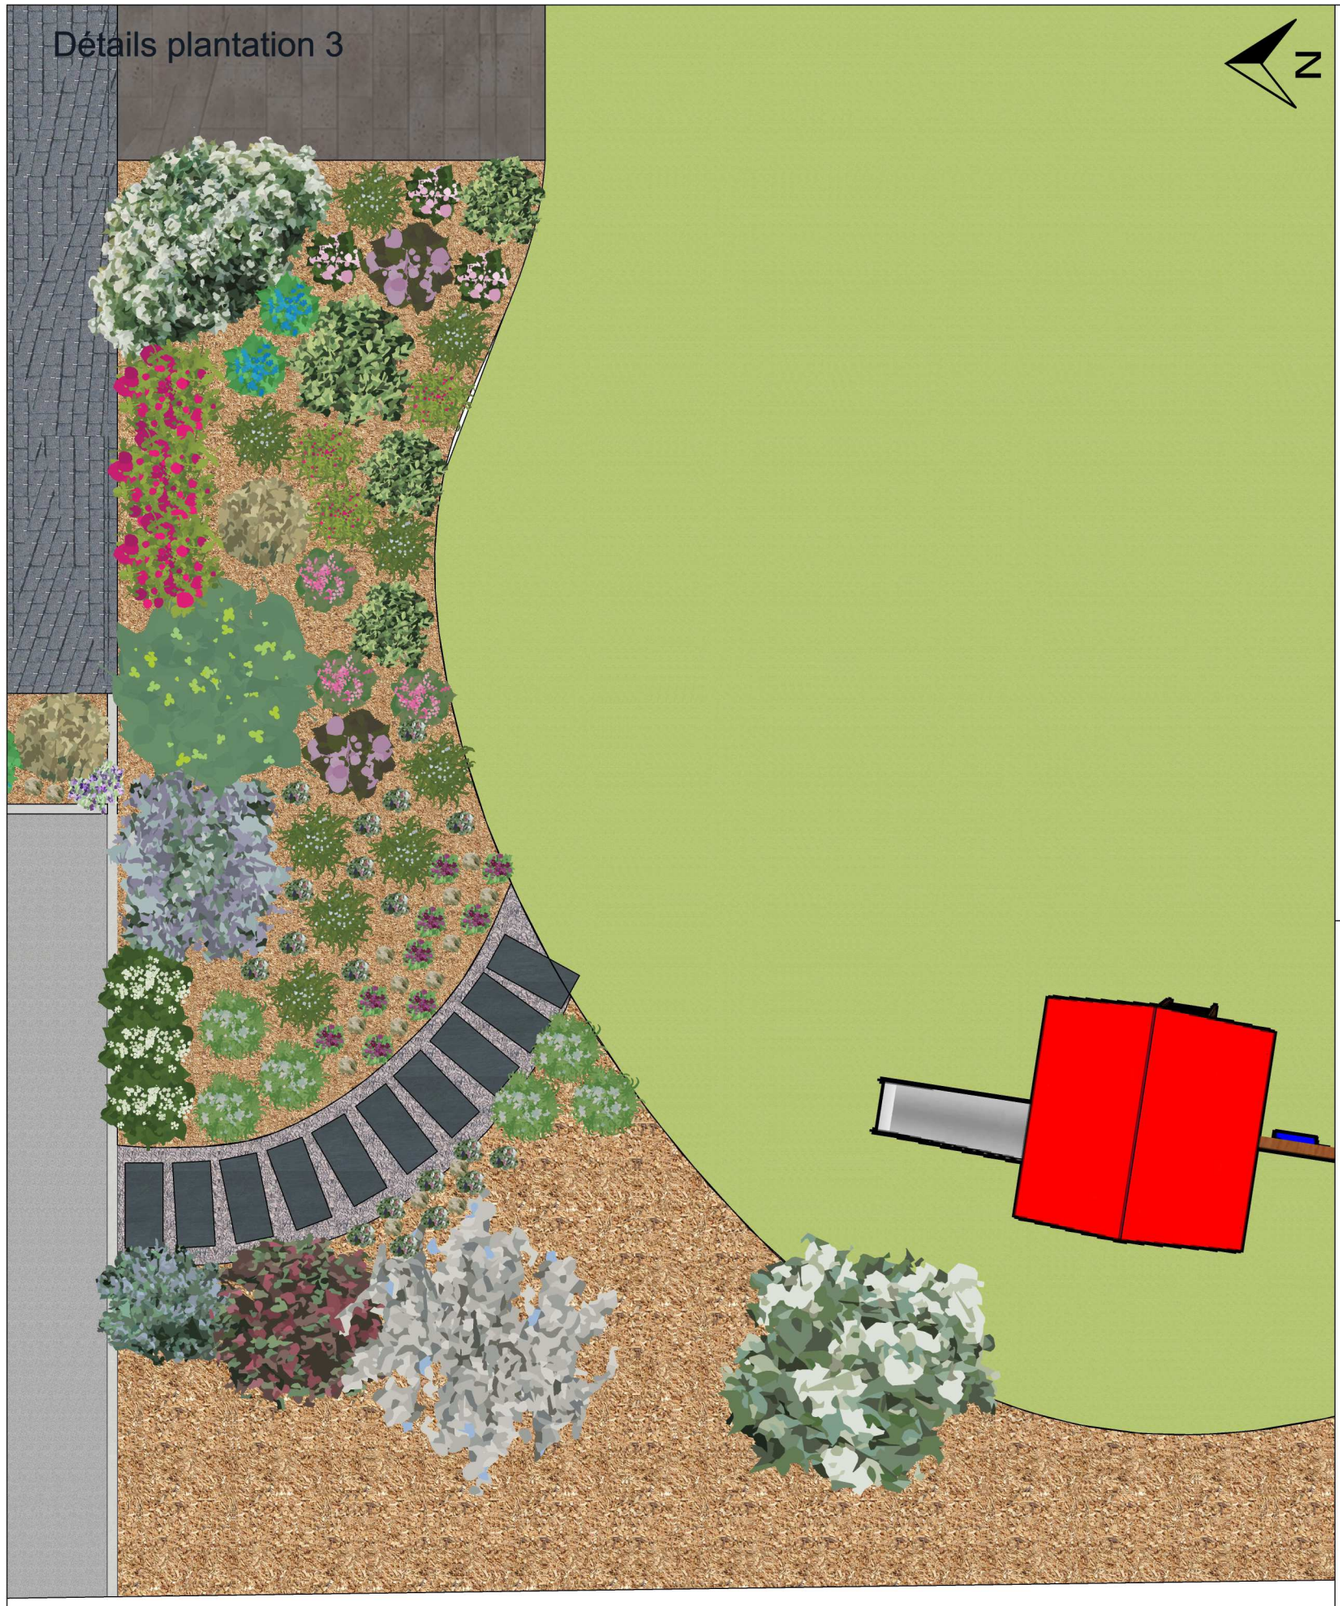

Massif anglais

1	Rosier Grimpant PALAIS ROYAL ® Meiviowit
3	Achillea millefolium 'Summer Wine',Achillée millefolium Summer Wine
1	Amelanchier canadensis,Amélanchier du Canada
3	Astilbe arendsii 'Anita Pfeifer' ,Astilbe rose Anita Pfeifer
1	Stipa gigantea,Avoine géante
4	Ilex crenata 'Convexa' ou 'Maximo'
14	Stipa tenuifolia,Cheveux d'ange
1	Ceanothus x delilianus 'Gloire de Versailles',Céanothe Gloire de Versailles
1	Ribes sanguineum 'King Edward VII'',Groseillier à fleurs
9	Pennisetum orientale,Herbe aux écouvillons
6	Hosta sieboldiana 'Elegans',Hosta à grandes feuilles
2	Lavatera thuringiaca 'Barnsley',Lavatère de Thuringe Barnsley
1	Choisya ternata,Oranger du Mexique
1	Osmanthus heterophyllus,Osmanthe à feuilles variables
19	Delphinium hybrides,Pied d'Alouette vivace
3	Paeonia 'duchessede Morny',Pivoine arbustive
3	Lythrum salicaria,Salicaire Rose Queen
2	Salvia uliginosa,Sauge
1	Philadelphus coronarius,Seringat
9	Tulipes à fleurs de pivoine 'Angélique'

	LA FABRIQUE DE JARDIN laurenpaysage@gmail.com www.lafabriquedejardins.fr	Projet de	- MORLAAS (64)	
	MASSIF ANGLAIS	Dessiné par : Laurence.B	Date : 27/03/2018	Echelle : 1:50

Planche photos massif anglais

Qté : 3

Décorosier grimpant 4 -

Qté : 3

Achillea millefolium 'Summer Wine' - Achillé

Qté : 1

Amelanchier canadensis - Amélanchier du Canada

Qté : 1

Vitex agnus castus - Arbre au poivre

Qté : 3

Astilbe arendsii 'Anita Pfeifer' - Asti

Qté : 1

Stipa gigantea - Avoine géante

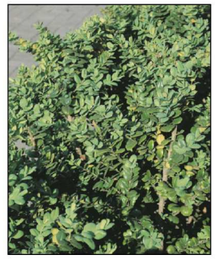

Qté : 3

Buxus sempervirens 'Rotundifolia' - Buis c

Qté : 14

Stipa tenuifolia - Cheveux d'ange

Qté : 1

Ceanothus x delilianus 'Gloire de Versailles'

Qté : 1

Ribes sanguineum 'King Edward VII" - Groseill

Qté : 9

Pennisetum orientale - Herbe aux écouvillons

Qté : 8

Hosta sieboldiana 'Elegans' - Hosta à gra

Qté : 2

Lavatera thuringiaca 'Barnsley' - Lavatère d

Qté : 1

Choisya ternata - Oranger du Mexique

Qté : 1

Osmanthus heterophyllus - Osmanth

Qté : 10

Delphinium hybrides - Pied d'Alouette vivace

Qté : 3

Paeonia 'duchessede Morny' - Pivoine arbust

Qté : 3

Lythrum virgatum 'Rose Queen' - Salicaire Rose

Qté : 2

Salvia uliginosa - Sauge

Qté : 1

Philadelphus coronarius - Seringat

Qté : 9

Tulipa 'Wonderful' - Tulipe Wonderful

LA FABRIQUE DE JARDIN laurenpaysage@gmail.com www.lafabriquedejardins.fr	Projet de	- MORLAAS (64)	
Planche photo	Dessiné par : Laurence.B	Date : 27/03/2018	Echelle :

Massif anglais

ALLEE DALLE DE SCHISTE ET GRAVIER BLANCE

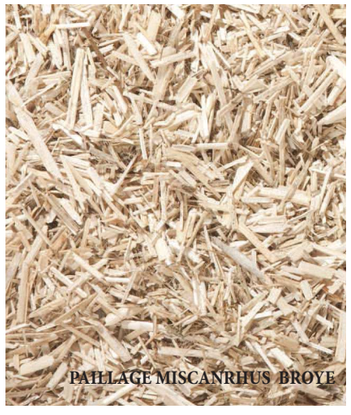

PAILLAGE MISCANRHUS BROYE

Projet d'aménagement paysager de
Mme et M
64160 MORLAAS

Planche d'ambiance 2

Laurence BAZEAU
07 72 43 27 00
laurenpaysage@gmail.fr

www.lafabriquedejardins.fr

n°siret : 835 118 019 00016

Détail plantations 1

Qté : 3

Dryopteris namegatae –

Qté : 3

Acanthus spinosus – Acanthe épineuse

Qté : 3

Astilbe japonica 'Gladstone' – Astilbe d

Qté : 2

Musa basjoo – Bananier du Japon

Qté : 3

Hosta fortunei 'albopicta' – Hosta for

Qté : 3

Iris ensata – Iris du Japon

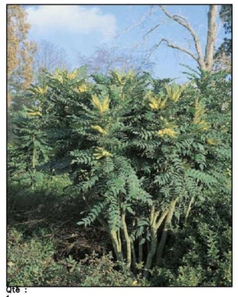

Qté : 1

Mahonia x media 'Charity' – Mahonia hyb

Qté : 1

Gunnera tinctoria – Rhubarbe géante du Chil

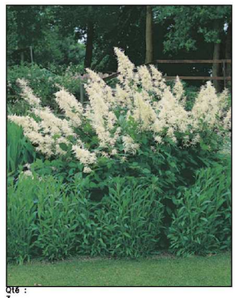

Qté : 3

Aruncus dioicus – Barbe-de-bouc

Qté : 1

Euphorbia schillingii – Euphorbe – Népal

Qté : 3

Fargesia nitida – Fragesia luisant

Qté : 5

Geranium 'orion' ou 'brookside' – Géranium

Qté : 3

Salvia involucrata 'berthellii' – Sauge –

Qté : 5

Salvia patens – Sauge gentiane

LA FABRIQUE DE JARDIN
laurenpaysage@gmail.com
www.lafabriquedejardins.fr

PLAN DE REVETEMENT	Projet de	- MORLAAS (64)	
	Dessiné par : Laurence.B	Date : 27/03/2018	Echelle : 1:25

Coin terrasse - Massif tropical

Source : Le clos du coudray - Jean Le Bret

CLAUSTRA ALU - Brand conception

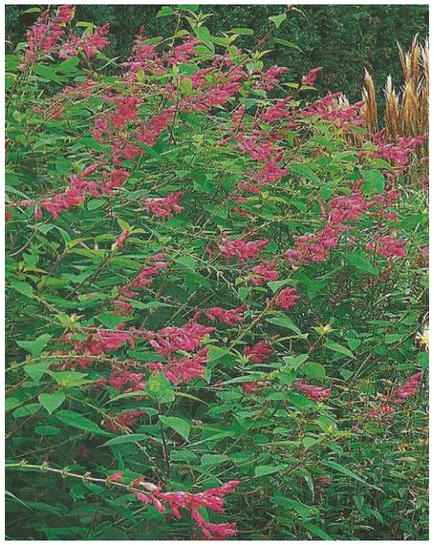

PAILAGE ECORCE DE PIN

Source : Le clos du coudray - Jean Le Bret

TERRASSE DALLE DE SCHISTE

MURET TRAVERSE CHEMIN DE FER

Projet d'aménagement paysager de
Mme et M
64160 MORLAAS

Planche d'ambiance 3

Laurence BAZEAU
07 72 43 27 00
laurenpaysage@gmail.fr

www.lafabriquedejardins.fr

n°siret : 835 118 019 00016